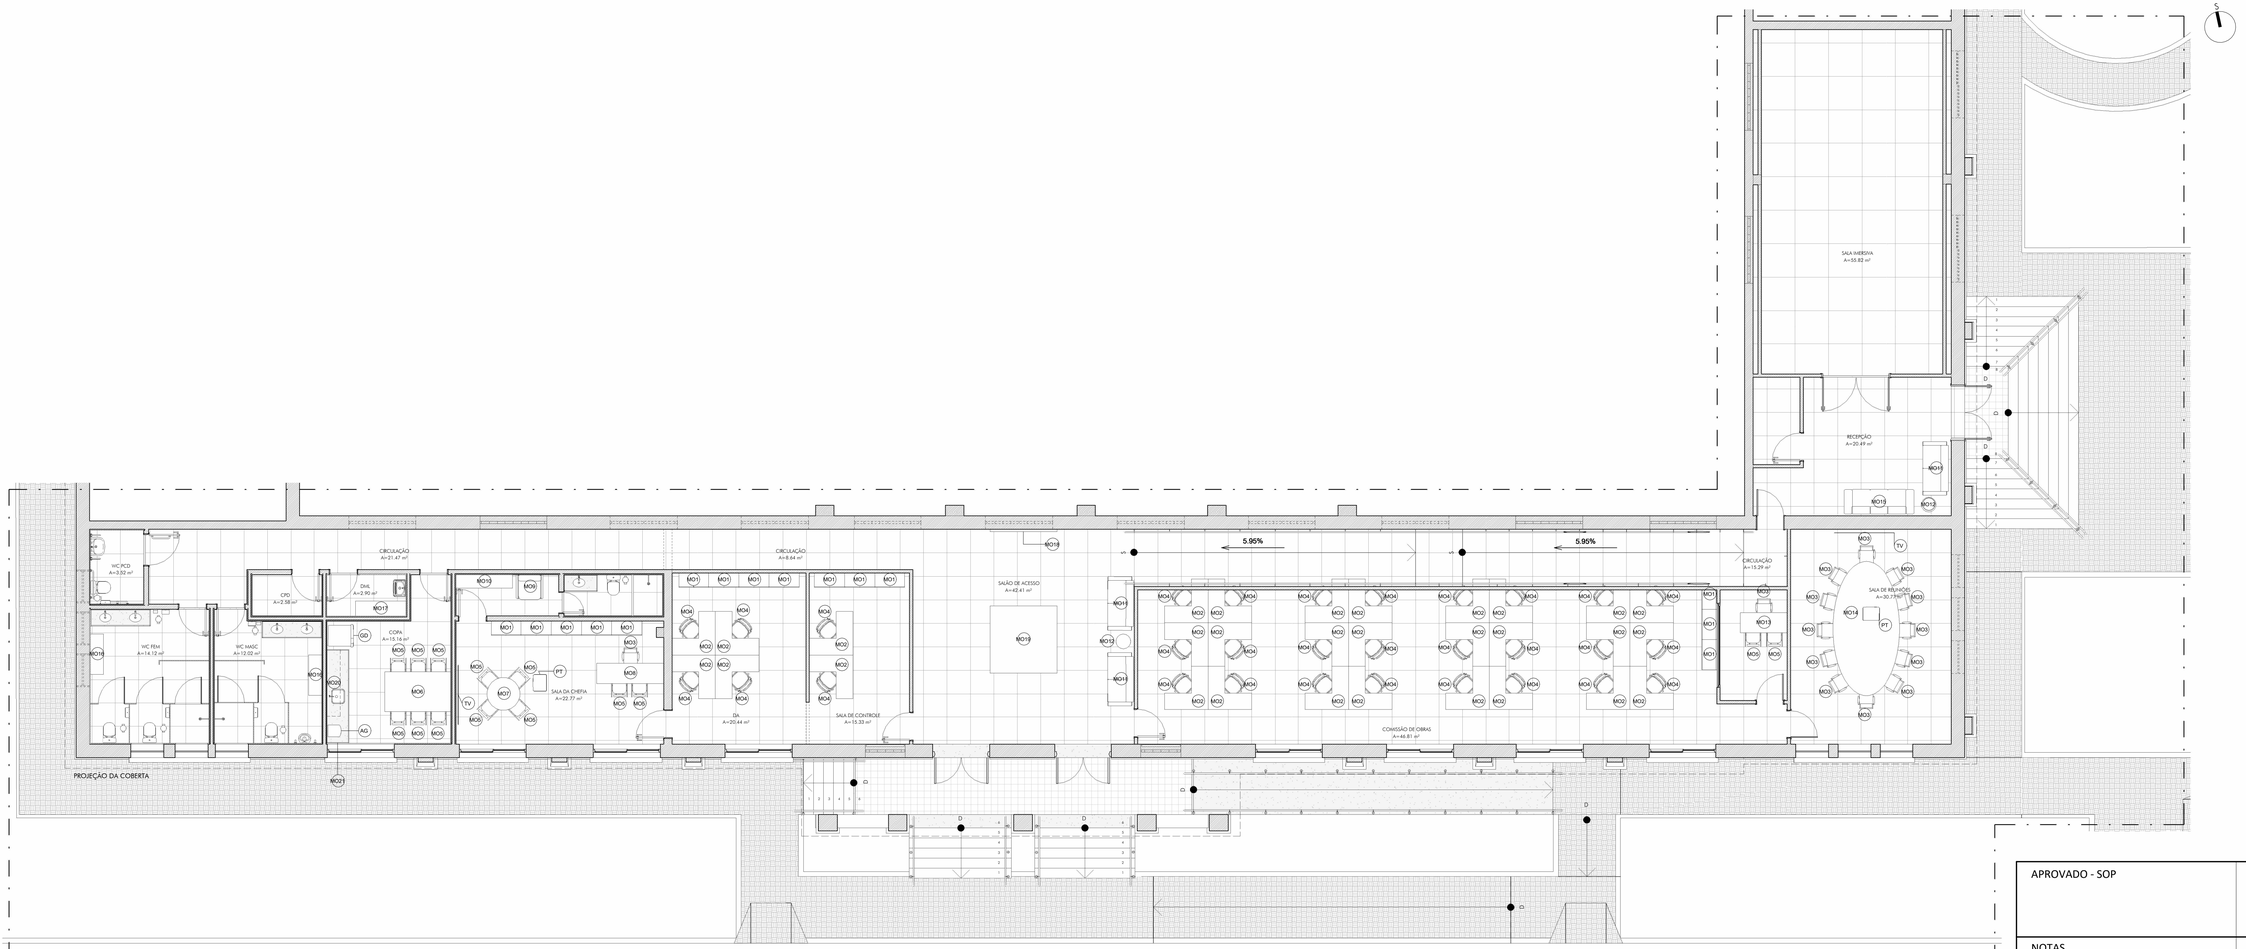


1 PL. BAIXA - LEIAUTE

ESC.: 1 : 75

Tabela de mobiliário

LEG	DESCRIÇÃO	QTDE
EQUIPAMENTO		
AG	PURIFICADOR DE ÁGUA	1
GD	GELADEIRA COM FREEZER	1
PT	PROJETOR DE TETO	2
TV	TV 85"	2
MOBILIÁRIO		
MO1	ARMÁRIO COM DUAS PORTAS DE ABRIR, MEDINDO 850 X 900 X 450 MM, CONFECCIONADO EM MDP DE 18MM, TAMPOSUPERIOR EM MDP DE 25 MM COM UMA PRATELEIRA	185
MO2	MESA EM L - DIMENSÕES 1300/1300X500X740MM (MODELO DA ATA)	30
MO3	CADEIRA COM ENCOSTO DE MOLDADO ANATOMICAMENTE COM BASE GIRATÓRIA SOBRE RODIZIOS COM BRAÇOS E ESPALDAR ALTO	14
MO4	CADEIRA COM ENCOSTO DE MOLDADO ANATOMICAMENTE COM BASE GIRATÓRIA SOBRE RODIZIOS SEM BRAÇO COM ESPALDAR MÉDIO	30
MO5	CADEIRA SEM RODIZIO SEM BRAÇO COM ESPALDAR BAIXO	14
MO6	MESA DE DIMENSÕES 2,0M X 1,2M X 0,85M - ESTRUTURA DE METAL E TAMPO DE LAMINADO MELAMÍNICO DE ALTA PRESSÃO.	1
MO7	MESA REDONDA DIÂMETRO 1,0M	1
MO8	MESA DE DIMENSÕES 2,0M X 0,6M X 0,85M - ESTRUTURA DE METAL E TAMPO DE LAMINADO MELAMÍNICO DE ALTA PRESSÃO.	1
MO9	POLTRONA	1
MO10	ARMÁRIO	1
MO11	SOFÁ DE 02 LUGARES	3
MO12	MESA CIRCULAR PARA APOIO, 35cm, h= 50cm	2
MO13	MESA DE DIMENSÕES 1,4M X 0,6M X 0,85M - ESTRUTURA DE METAL E TAMPO DE LAMINADO MELAMÍNICO DE ALTA PRESSÃO.	1
MO14	MESA COM TAMPO OVAL 2,0X1,0X0,85M	1
MO15	SOFÁ DE 03 LUGARES	1
MO16	BANCO DE MADEIRA DE APOIO	2
MO17	ESTANTE DE APOIO	1
MO18	PAINEL DE FOTOS	1
MO19	MAQUETE FÍSICA DA BASE AÉREA	1
MO20	ARMÁRIO SUPERIOR EM MDF, COM REVESTIMENTO EM LAMINADO MELAMÍNICO, DIM.: 2,00x0,75x0,40	1
MO21	ARMÁRIO EM MDF HIDRÓFUGO, ESPESSURA 20mm, ULTRA PREMIUM DURATEX OU SIMILAR, COM REVESTIMENTO EM LAMINADO MELAMÍNICO NA COR BRANCO COM PUXADORES EM PERFIL DE ALUMÍNIO NATURAL	1
		129

APROVADO - SOP

APROVADO - COFZ

NOTAS

01. Todas as medidas deste documento estão em metro.
02. Conferir escalas indicadas no desenho.
03. Em caso de dúvida, entrar em contato com o(s) arquiteto(s) responsável(eis).
04. As coordenadas, caso existentes, são extraídas do levantamento topográfico.
05. Conferir medidas in loco para execução de esquadrias, vidros e bancadas.
06. O escritório não se responsabiliza por alterações de projeto ou soluções executadas sem conhecimento dos arquitetos responsáveis.
07. Todas as plantas possuem indicações para o SUL.

PROPRIETÁRIO

PROJETO

CÁLCULO

CONSTRUÇÃO

REV.	DESCRIÇÃO	DATA
R06	EMISSÃO INICIAL	08/2025
R01	Demolir/Construir escada externa; Acréscimo de sala técnica	10/10/2025
R02	Revisão de detalhamento	17/10/2025
R03	Ajustes de janelas / Forros	05/11/2025
R04	Revisão de detalhamento	03/12/2025
R05	Revisão de anotações e acréscimo de planta de coberta	10/12/2025
R06	Revisão de sala imersiva	10/12/2025

PROJETO ITA / CAMPUS FORTALEZA, CEARÁ - 2ª ETAPA

DISCIPLINA
ARQUITETURA

FASE
PROJETO EXECUTIVO

EDIFÍCIO
E-65 CO-FZ-COP

CONTEÚDO
PLANTA DE LAYOUT

ARQUIVO
MODELO **CE01-01PE02-ARQ-R06**
PRANCHA **CE01-01PE02-ARQ-DE009-R06**

ESCALA	UNIDADE	PRANCHA
IND.	m	**009/022**

RESPONSÁVEL TÉCNICO

GEORGE LINS
CAU A48586-1

EQUIPE		ESTAGIÁRIOS
CINTIA LINS	CAU A104193-2	BEATRIZ VIEIRA
KELMA PINHEIRO	CAU A34582-2	ELIAS PORTELA
KELSYO SOUSA	CAU A318850-0	SÁVIO MARTINS
LARISSA RIBEIRO	CAU A313220-0	
NAILA PAIVA	CAU A133213-9	
PEDRO SANTOS	CAU A188138-8	
THAÍZA RICARTE	CAU A139510-6	
YUKA OGAWA	CAU A248654-7	

Construtora Porto · CONSTRUTORA CETRO · Construtora Morais Vasconcelos Desde 1979

CONSÓRCIO CETRO/PORTO/MORAIS - ITA 2ª ETAPA

09/03/2026 14:35:16