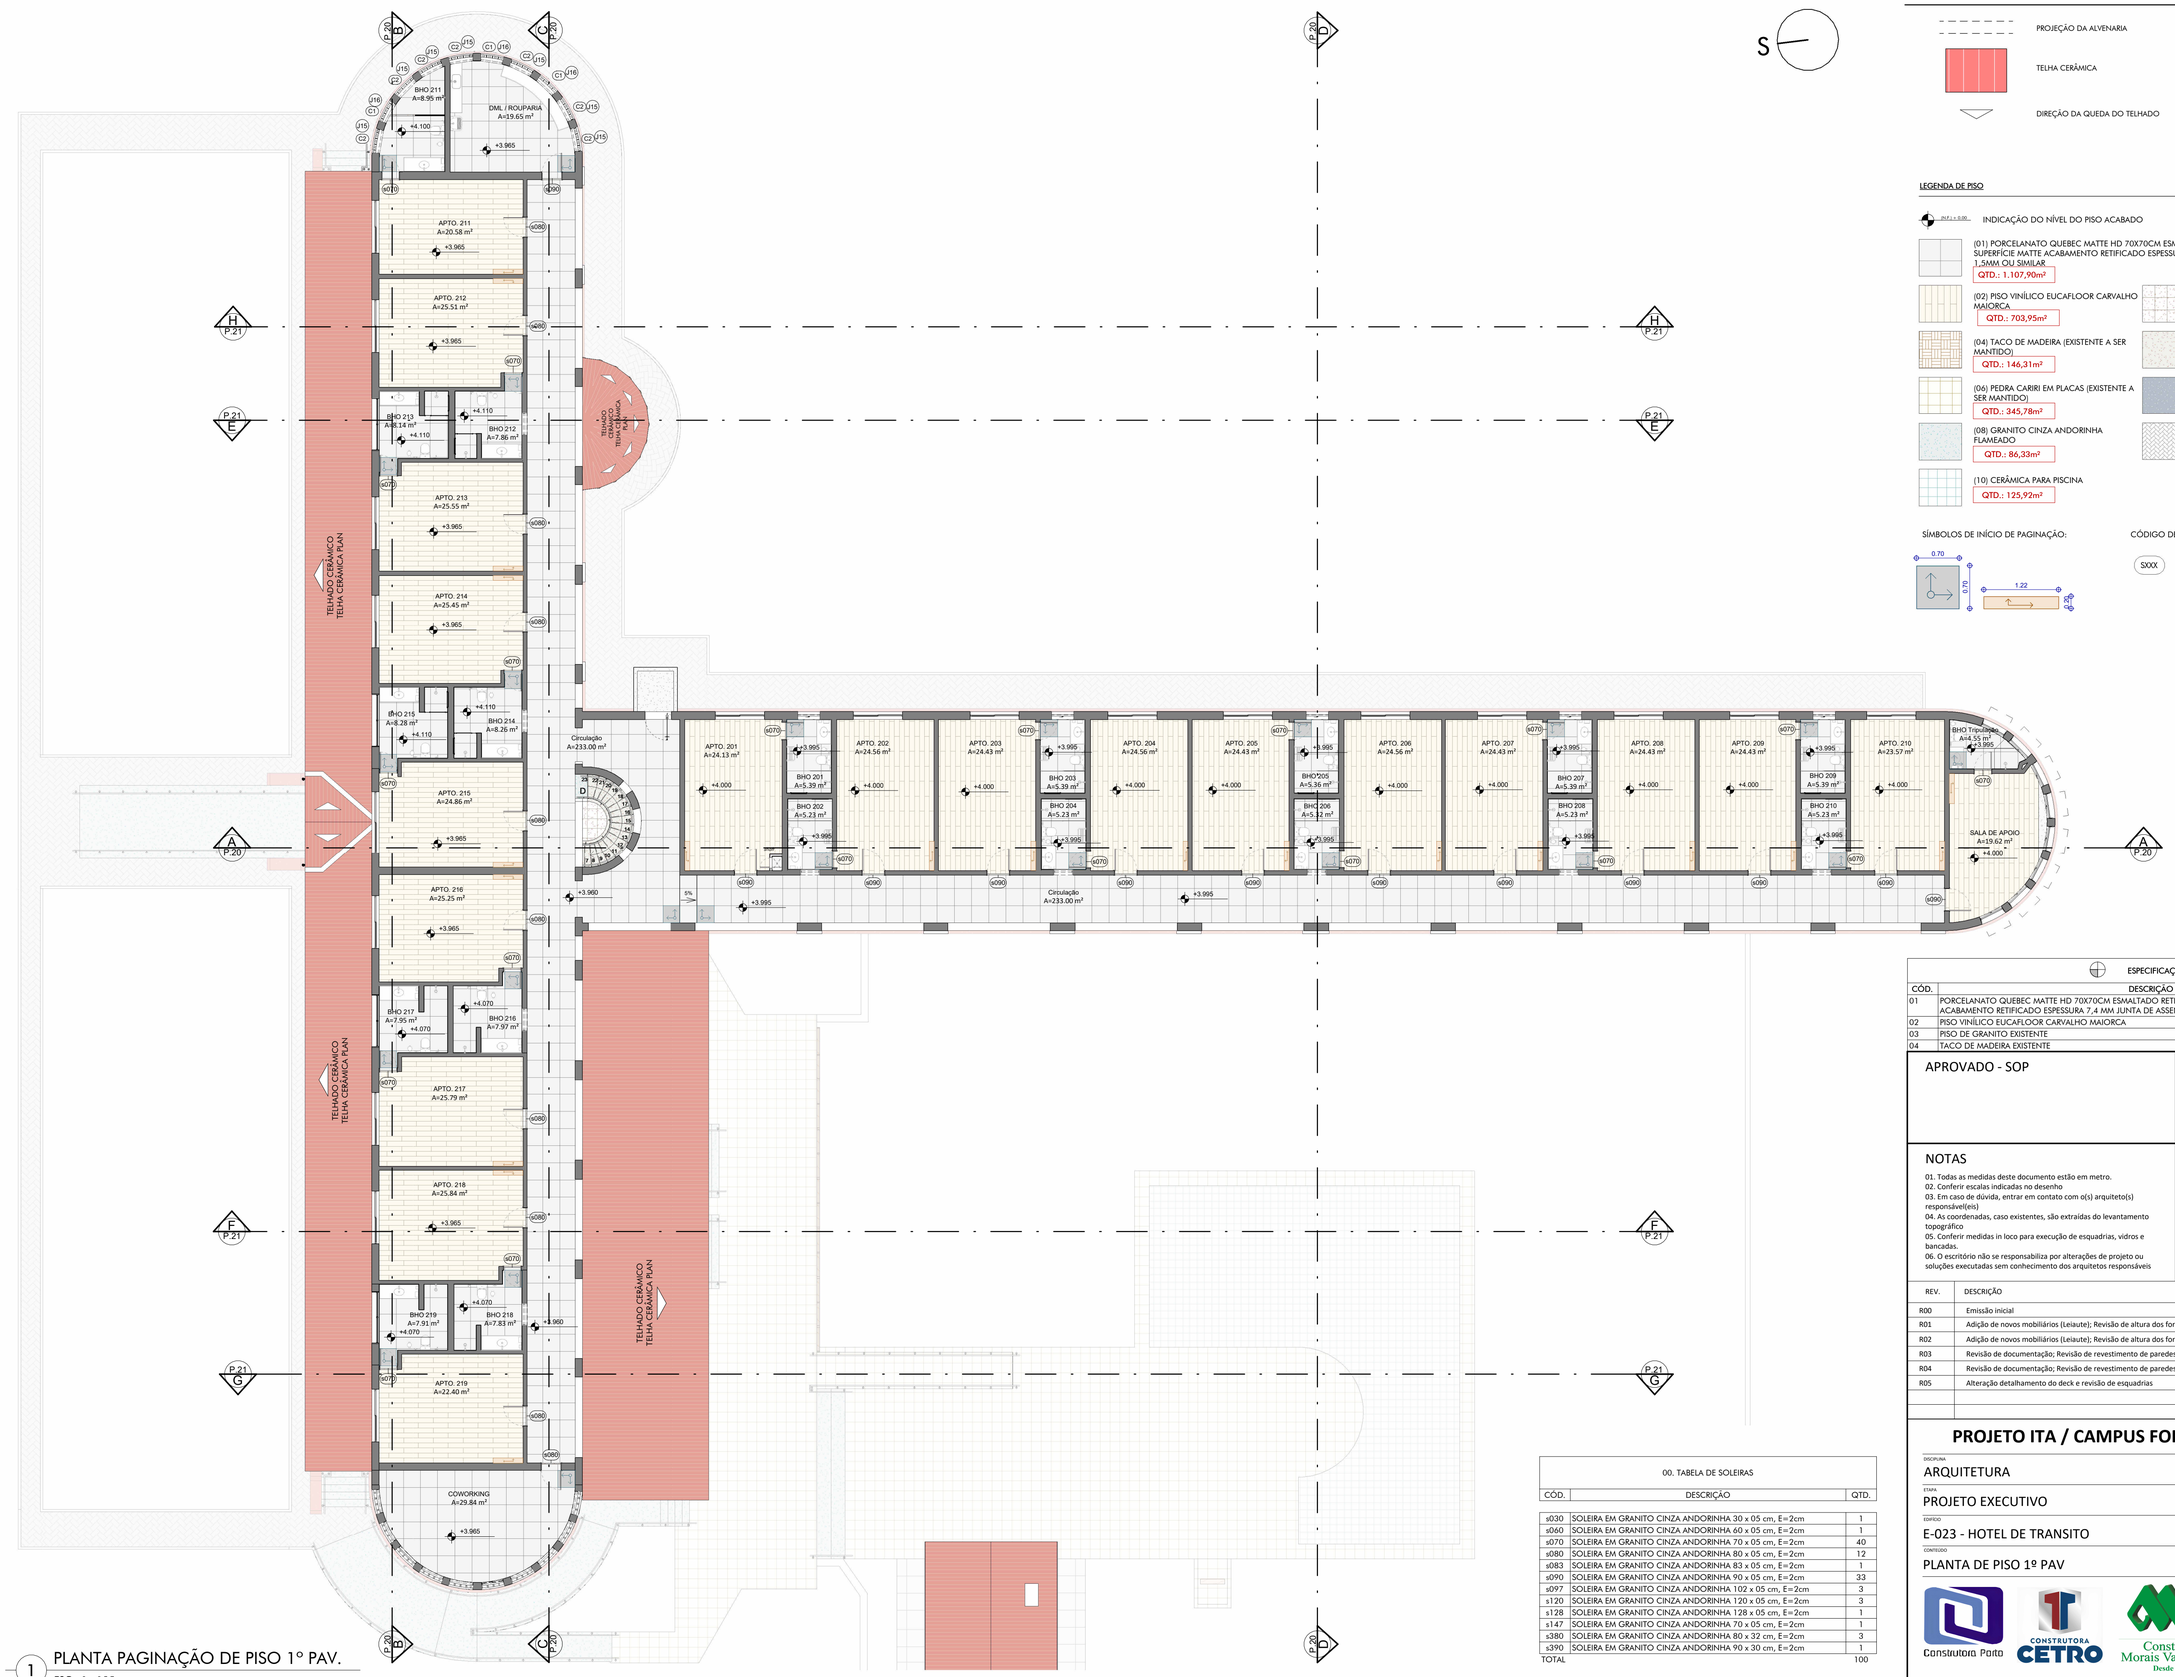


1 PLANTA PAGINAÇÃO DE PISO 1º PAV.
ESC.: 1 : 125

S

LEGENDA DE COBERTA

PROJEÇÃO DA ALVENARIA

TELHA CERÂMICA

DIREÇÃO DA QUEDA DO TELHADO

LEGENDA DE PISO

INDICAÇÃO DO NÍVEL DO PISO ACABADO

(01) PORCELANATO QUEBEC MATTE HD 70X70CM ESMALTADO RETIFICADO LINHA URBAN SUPERFÍCIE MATTE ACABAMENTO RETIFICADO ESPESSURA 7,4 MM JUNTA DE ASSENTAMENTO 1,5MM OU SIMILAR
QTD.: 1.107,90m²

(02) PISO VINÍLICO EUCAFLOOR CARVALHO MAIORCA
QTD.: 703,95m²

(03) GRANITO POLIDO EM PLACAS (EXISTENTE A SER MANTIDO)
QTD.: 1.107,90m²

(04) TACO DE MADEIRA (EXISTENTE A SER MANTIDO)
QTD.: 146,31m²

(05) GRANITO CINZA ANDORINHA POLIDO
QTD.: 4,30m²

(06) PEDRA CARIRI EM PLACAS (EXISTENTE A SER MANTIDO)
QTD.: 345,78m²

(07) GRANITO PRETO SÃO GABRIEL POLIDO (EXISTENTE A SER MANIDO
QTD.: 1,19m²

(08) GRANITO CINZA ANDORINHA FLAMEADO
QTD.: 86,33m²

(09) BLOCO INTERTRAVADO RETANGULAR DE CONCRETO COR NATURAL - PAVIMENTO PARA PEDESTRES
QTD.: 293,29m²

(10) CERÂMICA PARA PISCINA
QTD.: 125,92m²

SÍMBOLOS DE INÍCIO DE PAGINAÇÃO:

CÓDIGO DE IDENTIFICAÇÃO DE SOLEIRAS:

SXXX

00. TABELA DE SOLEIRAS

CÓD.	DESCRIÇÃO	QTD.
s030	SOLEIRA EM GRANITO CINZA ANDORINHA 30 x 05 cm, E=2cm	1
s060	SOLEIRA EM GRANITO CINZA ANDORINHA 60 x 05 cm, E=2cm	1
s070	SOLEIRA EM GRANITO CINZA ANDORINHA 70 x 05 cm, E=2cm	40
s080	SOLEIRA EM GRANITO CINZA ANDORINHA 80 x 05 cm, E=2cm	12
s083	SOLEIRA EM GRANITO CINZA ANDORINHA 83 x 05 cm, E=2cm	1
s090	SOLEIRA EM GRANITO CINZA ANDORINHA 90 x 05 cm, E=2cm	33
s097	SOLEIRA EM GRANITO CINZA ANDORINHA 102 x 05 cm, E=2cm	3
s120	SOLEIRA EM GRANITO CINZA ANDORINHA 120 x 05 cm, E=2cm	3
s128	SOLEIRA EM GRANITO CINZA ANDORINHA 128 x 05 cm, E=2cm	1
s147	SOLEIRA EM GRANITO CINZA ANDORINHA 70 x 05 cm, E=2cm	1
s380	SOLEIRA EM GRANITO CINZA ANDORINHA 80 x 32 cm, E=2cm	3
s390	SOLEIRA EM GRANITO CINZA ANDORINHA 90 x 30 cm, E=2cm	1
TOTAL		100

ESPECIFICAÇÃO DE PISO

CÓD.	DESCRIÇÃO	QTD.
01	PORCELANATO QUEBEC MATTE HD 70X70CM ESMALTADO RETIFICADO LINHA URBAN SUPERFÍCIE MATTE ACABAMENTO RETIFICADO ESPESSURA 7,4 MM JUNTA DE ASSENTAMENTO 1,5MM OU SIMILAR	1.107,90m²
02	PISO VINÍLICO EUCAFLOOR CARVALHO MAIORCA	703,95m²
03	PISO DE GRANITO EXISTENTE	36,91m²
04	TACO DE MADEIRA EXISTENTE	146,31m²

APROVADO - SOP

APROVADO - COFZ

NOTAS

01. Todas as medidas deste documento estão em metro.
02. Conferir escalas indicadas no desenho
03. Em caso de dúvida, entrar em contato com o(s) arquiteto(s) responsável(eis)
04. As coordenadas, caso existentes, são extraídas do levantamento topográfico
05. Conferir medidas in loco para execução de esquadrias, vidros e bancadas.
06. O escritório não se responsabiliza por alterações de projeto ou soluções executadas sem conhecimento dos arquitetos responsáveis

PROPRIETÁRIO

PROJETO

CÁLCULO

CONSTRUÇÃO

REV.	DESCRIÇÃO	DATA
R00	Emissão inicial	22/12/2025
R01	Adição de novos mobiliários (Leiaute); Revisão de altura dos forros; Adição de Det. de rampas	16/01/2026
R02	Adição de novos mobiliários (Leiaute); Revisão de altura dos forros; Adição de Det. de rampas	02/02/2026
R03	Revisão de documentação; Revisão de revestimento de paredes	24/03/2026
R04	Revisão de documentação; Revisão de revestimento de paredes	08/04/2026
R05	Alteração detalhamento do deck e revisão de esquadrias	07/07/2026

PROJETO ITA / CAMPUS FORTALEZA, CEARÁ - 2ª ETAPA

DISCIPLINA
ARQUITETURA

ETAPA
PROJETO EXECUTIVO

EDIFÍCIO
E-023 - HOTEL DE TRANSITO

CONTEÚDO
PLANTA DE PISO 1º PAV

ARQUIVO
MODELO **CE01-14PE01-ARQ-R05**
PRANCHA **CE01-14PE01-ARQ-DE18-R05**

ESCALA | UNIDADE METRO | PRANCHA **18 /42**

RESPONSÁVEL TÉCNICO
GEORGE LINS
CAU A48586-1

EQUIPE		ESTAGIÁRIOS
CINTIA LINS	CAU A104193-2	BEATRIZ VIEIRA
KELMA PINHEIRO	CAU A34582-2	ELIAS PORTELA
KELSYO SOUSA	CAU A313850-0	SÁVIO MARTINS
LARISSA RIBEIRO	CAU A313220-0	
NAILA PAIVA	CAU A133213-9	
PEDRO SANTOS	CAU A188138-8	
THAIZA RICARTE	CAU A139510-6	
YUKA OGAWA	CAU A248654-7	

Construtora Porto · CONSTRUTORA CETRO · Construtora Morais Vasconcelos Desde 1979

CONSÓRCIO CETRO/PORTO/MORAIS - ITA 2ª ETAPA

07/07/2026 07:10:28